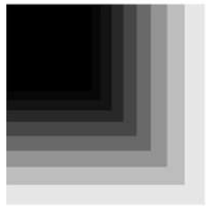

PROSPECT24

ԲՆԱԿԵԼԻ ՇԵՆՔԻ ԷՍՔԻԶԱՅԻՆ ՆԱԽԱԳԻԾ

ԿՈՏԱՅՔԻ ՄԱՐԶ, ՆԱԻՐԻ ՀԱՄԱՅՆՔ, ԳՅՈՒՂ ՔԱՍԱԽ, Վ ՍԱՐԳՍՅԱՆ 8/4

ԿԱԴԱՍՏՐԱՅԻՆ ԾԱԾԿԱԳՐԵՐ՝
07-065-0036-0001

ՊԱՏՎԻՐԱՏՈՒ՝
Հայաստանի Հանրապետություն

ԿԱՏԱՐՈՂՆԵՐ՝
ԱՇՈՏ ԽԱՉԱՏՈՒՐՅԱՆ
ՏԻԳՐԱՆ ՍԻՄՈՆՅԱՆ

ԿՈՆՏԱԿՏԱՅԻՆ ՏՎՅԱԼՆԵՐ՝
"KHACHATURIAN ARCHITECTS"
ԵՐԵՎԱՆ, ԱՄԻՐՅԱՆ 1
+374 41 250886
a@khachaturian.studio

ԱՆՎԱՆԱՑԱՆԿ

ԹԵՐԹԻ ԱՆՎԱՆՈՒՄ	ԷՋ
ԸՆԴՀԱՆՈՒՐ ՏԵՂԵԿՈՒԹՅՈՒՆ ԵՎ ԱՆՎԱՆԱՑԱՆԿ	*1*
ՀՈՂԱՄԱՍԻ ՍԻՏՈՒԱՑԻՈՆ ՀԱՏԱԿԱԳԻԾ	*2*
ԳՈՅՈՒԹՅՈՒՆ ՈՒՆԵՑՈՂ 1 ՀԱՐԿԻ ՀԱՏԱԿԱԳԻԾ	*3*
ԳՈՅՈՒԹՅՈՒՆ ՈՒՆԵՑՈՂ 2 ՀԱՐԿԻ ՀԱՏԱԿԱԳԻԾ	*4*
ԳԼԽԱՎՈՐ ՀԱՏԱԿԱԳԻԾ	*5*
ԱՌԱՋԱՐԿՎՈՂ 1 ՀԱՐԿԻ ՀԱՏԱԿԱԳԻԾ	*6*
ԱՌԱՋԱՐԿՎՈՂ 2 ՀԱՐԿԻ ՀԱՏԱԿԱԳԻԾ	*7*
ԱՌԱՋԱՐԿՎՈՂ 3 ՀԱՐԿԻ ՀԱՏԱԿԱԳԻԾ	*8*
ԳԼՂԱՎՈՐ ԵՎ ԲԱԿԱՅԻՆ ՃԱԿԱՏՆԵՐ	*9*
ԿՈՂԱՅԻՆ ՃԱԿԱՏՆԵՐ	*10*

ՏԵԽՆԻԿԱՏՆՏԵՍԱԿԱՆ ՑՈՒՑԱՆԻՇՆԵՐԻ ՑԱՆԿ

	ՑՈՒՑԱՆԻՇԻ ԱՆՎԱՆՈՒՄ	ՄԻԱՎՈՐ
1	*ՀՈՂԱՄԱՍԻ ՄԱԿԵՐԵՍ*	*8740 Մ^2*
2	*ՇԵՆՔԻ ՀԱՐԿԱՅՆՈՒԹՅՈՒՆ*	*3*
3	*ԿԱՌՈՒՑԱՊԱՏՄԱՆ ՄԱԿԵՐԵՍ*	*1040.8 Մ^2 (11.9%)*
4	*ԱՆՋՐԱԹԱՓԱՆՑ ՄԱԿԵՐԵՍ*	*3401.5 Մ^2 (38.9%)*
5	*ՎԵՐԳԵՏՆՅԱ ՀԱՐԿԵՐԻ ԸՆԴՀԱՆՈՒՐ ՄԱԿԵՐԵՍ*	*2380.6 Մ^2*
6	*ԱՎՏՈԿԱՅԱՆԱՏԵՂԵՐԻ ՔԱՆԱԿ*	*82*

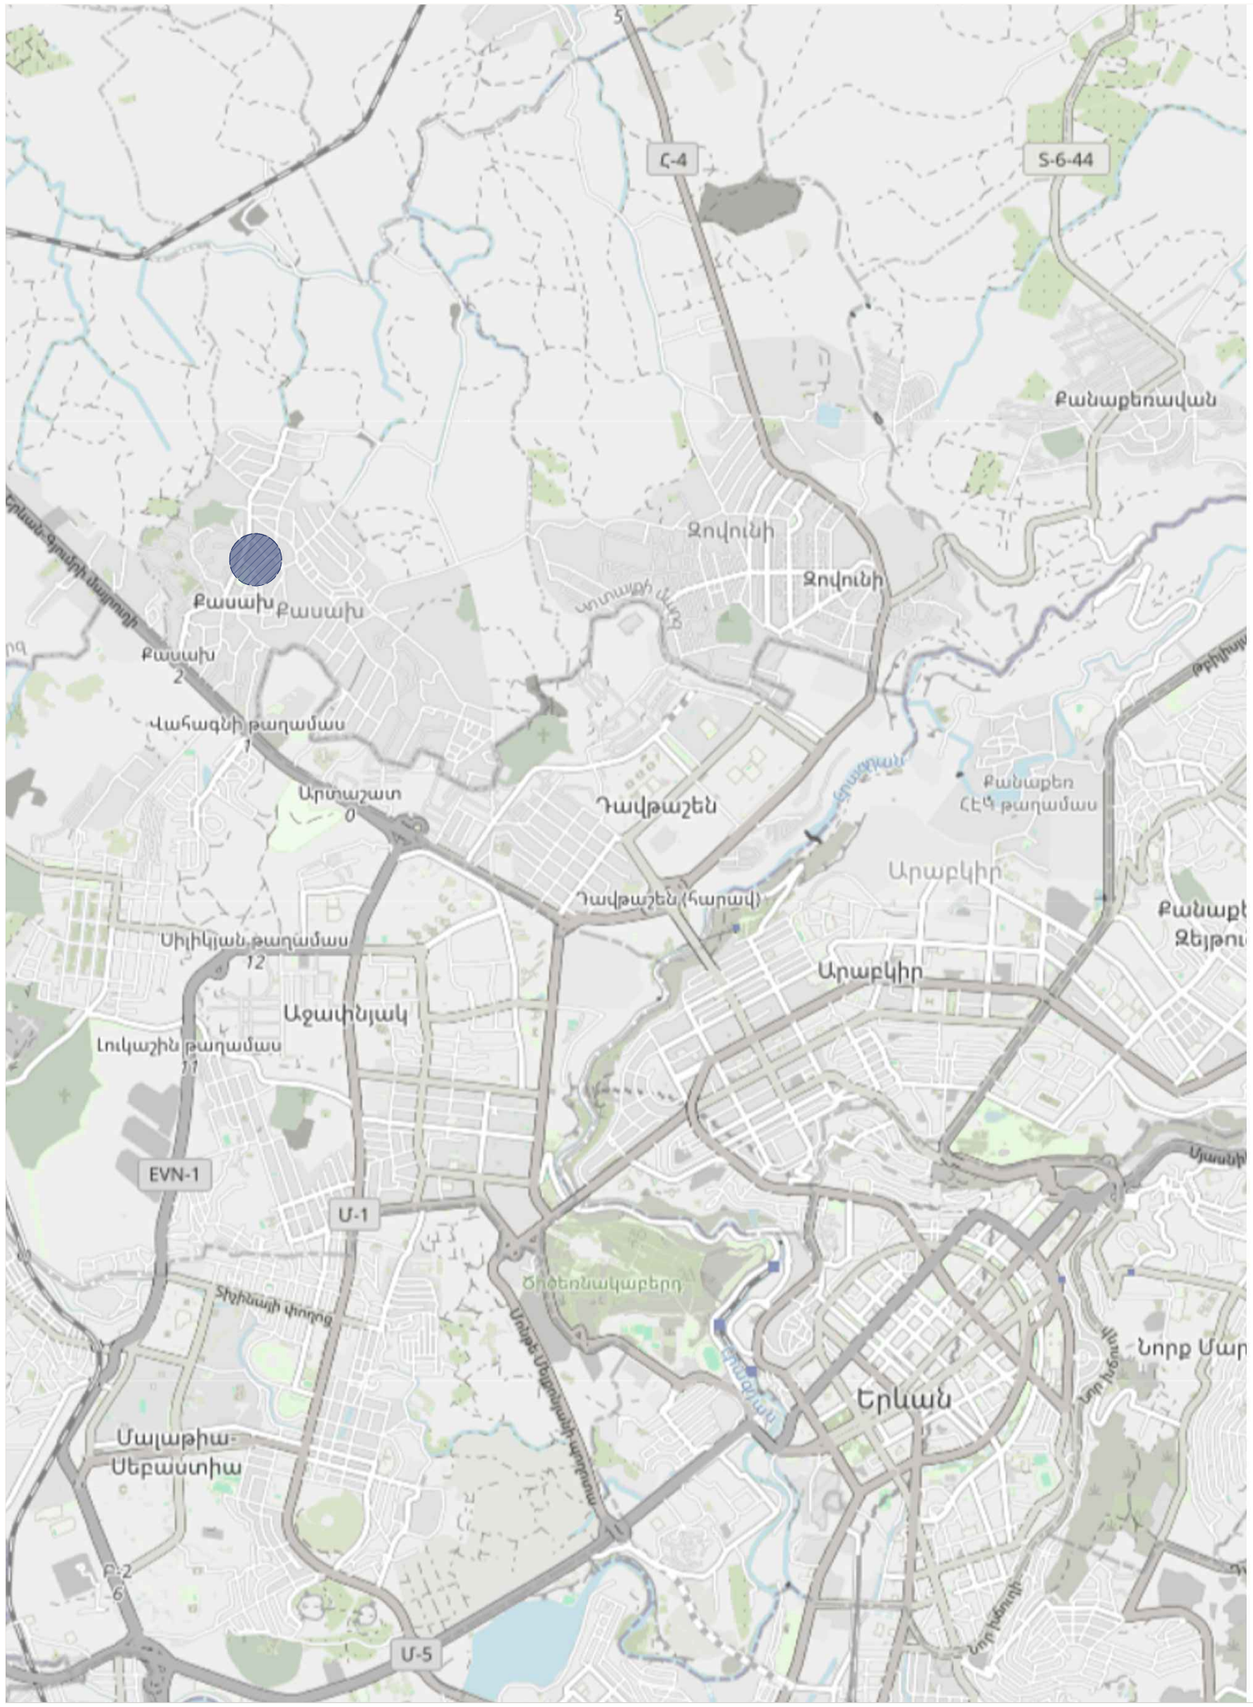

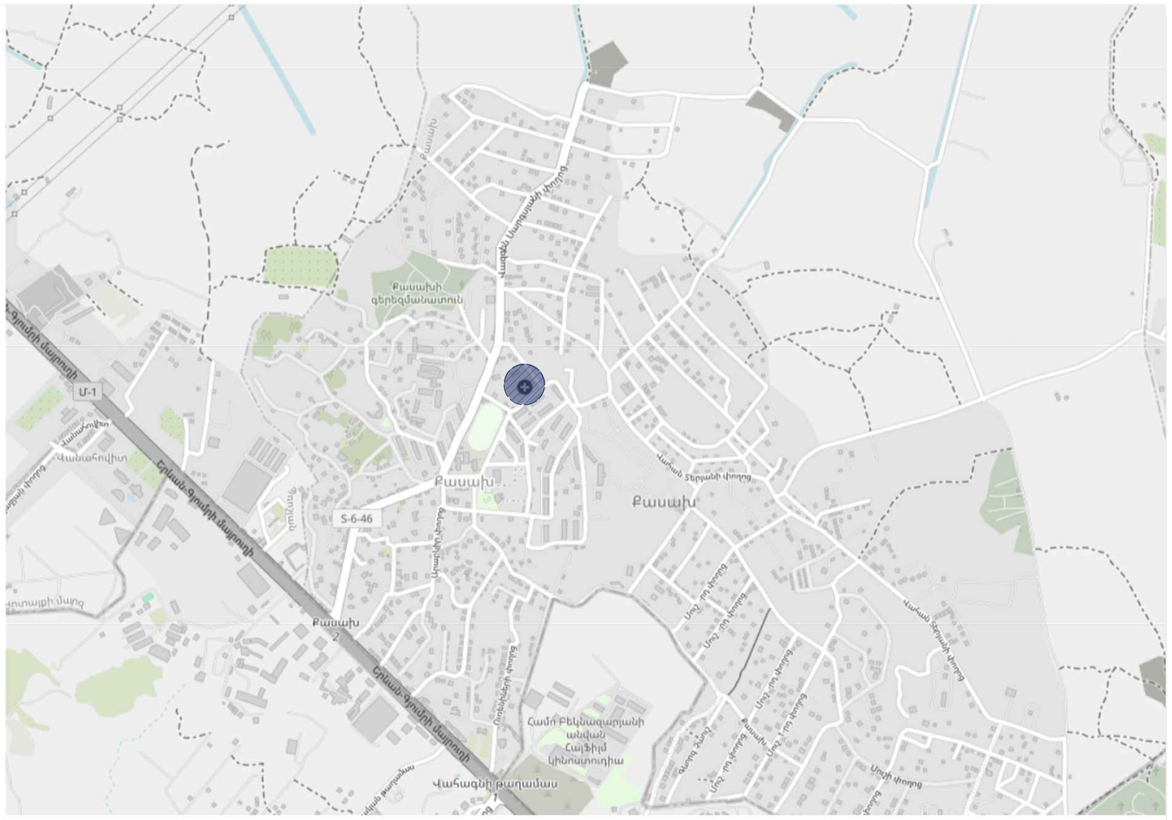

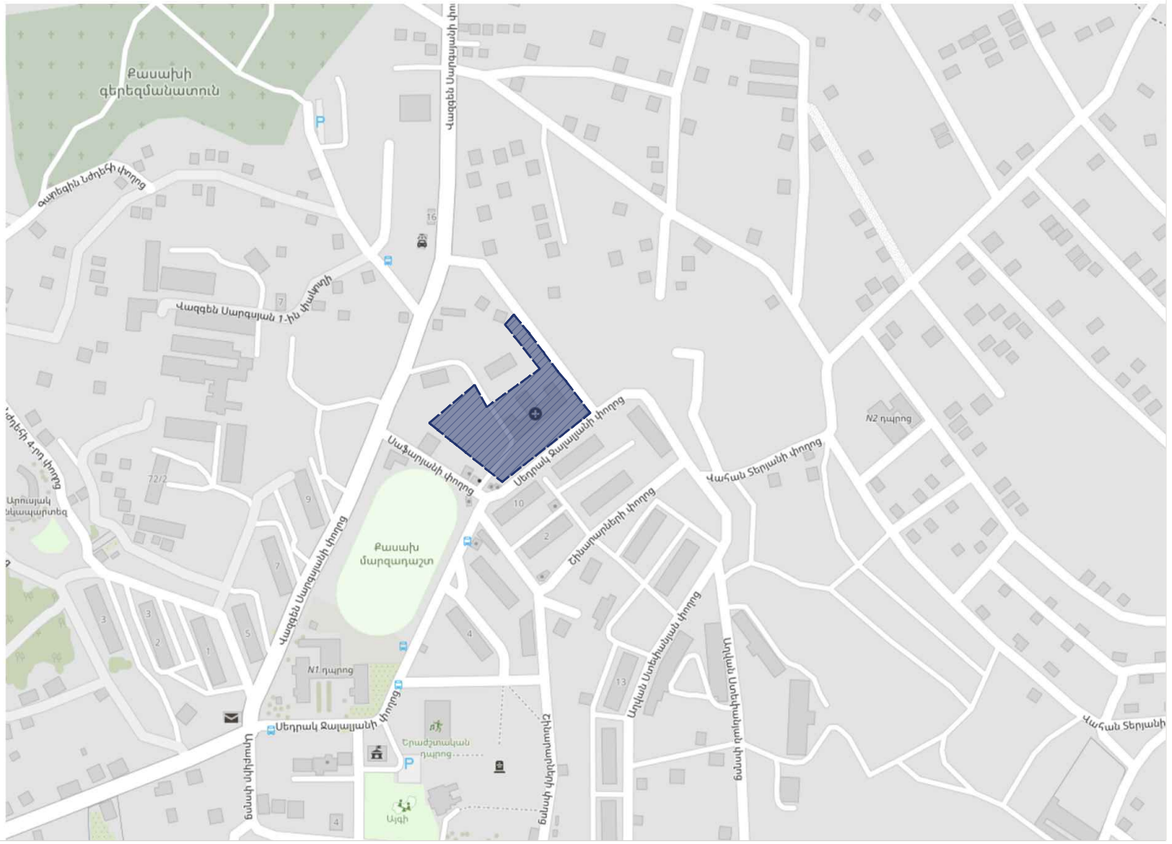

ԸՆԴՀԱՆՈՒՐ ՏԵՂԵԿՈՒԹՅՈՒՆ ԵՎ ԱՆՎԱՆԱՑԱՆԿ

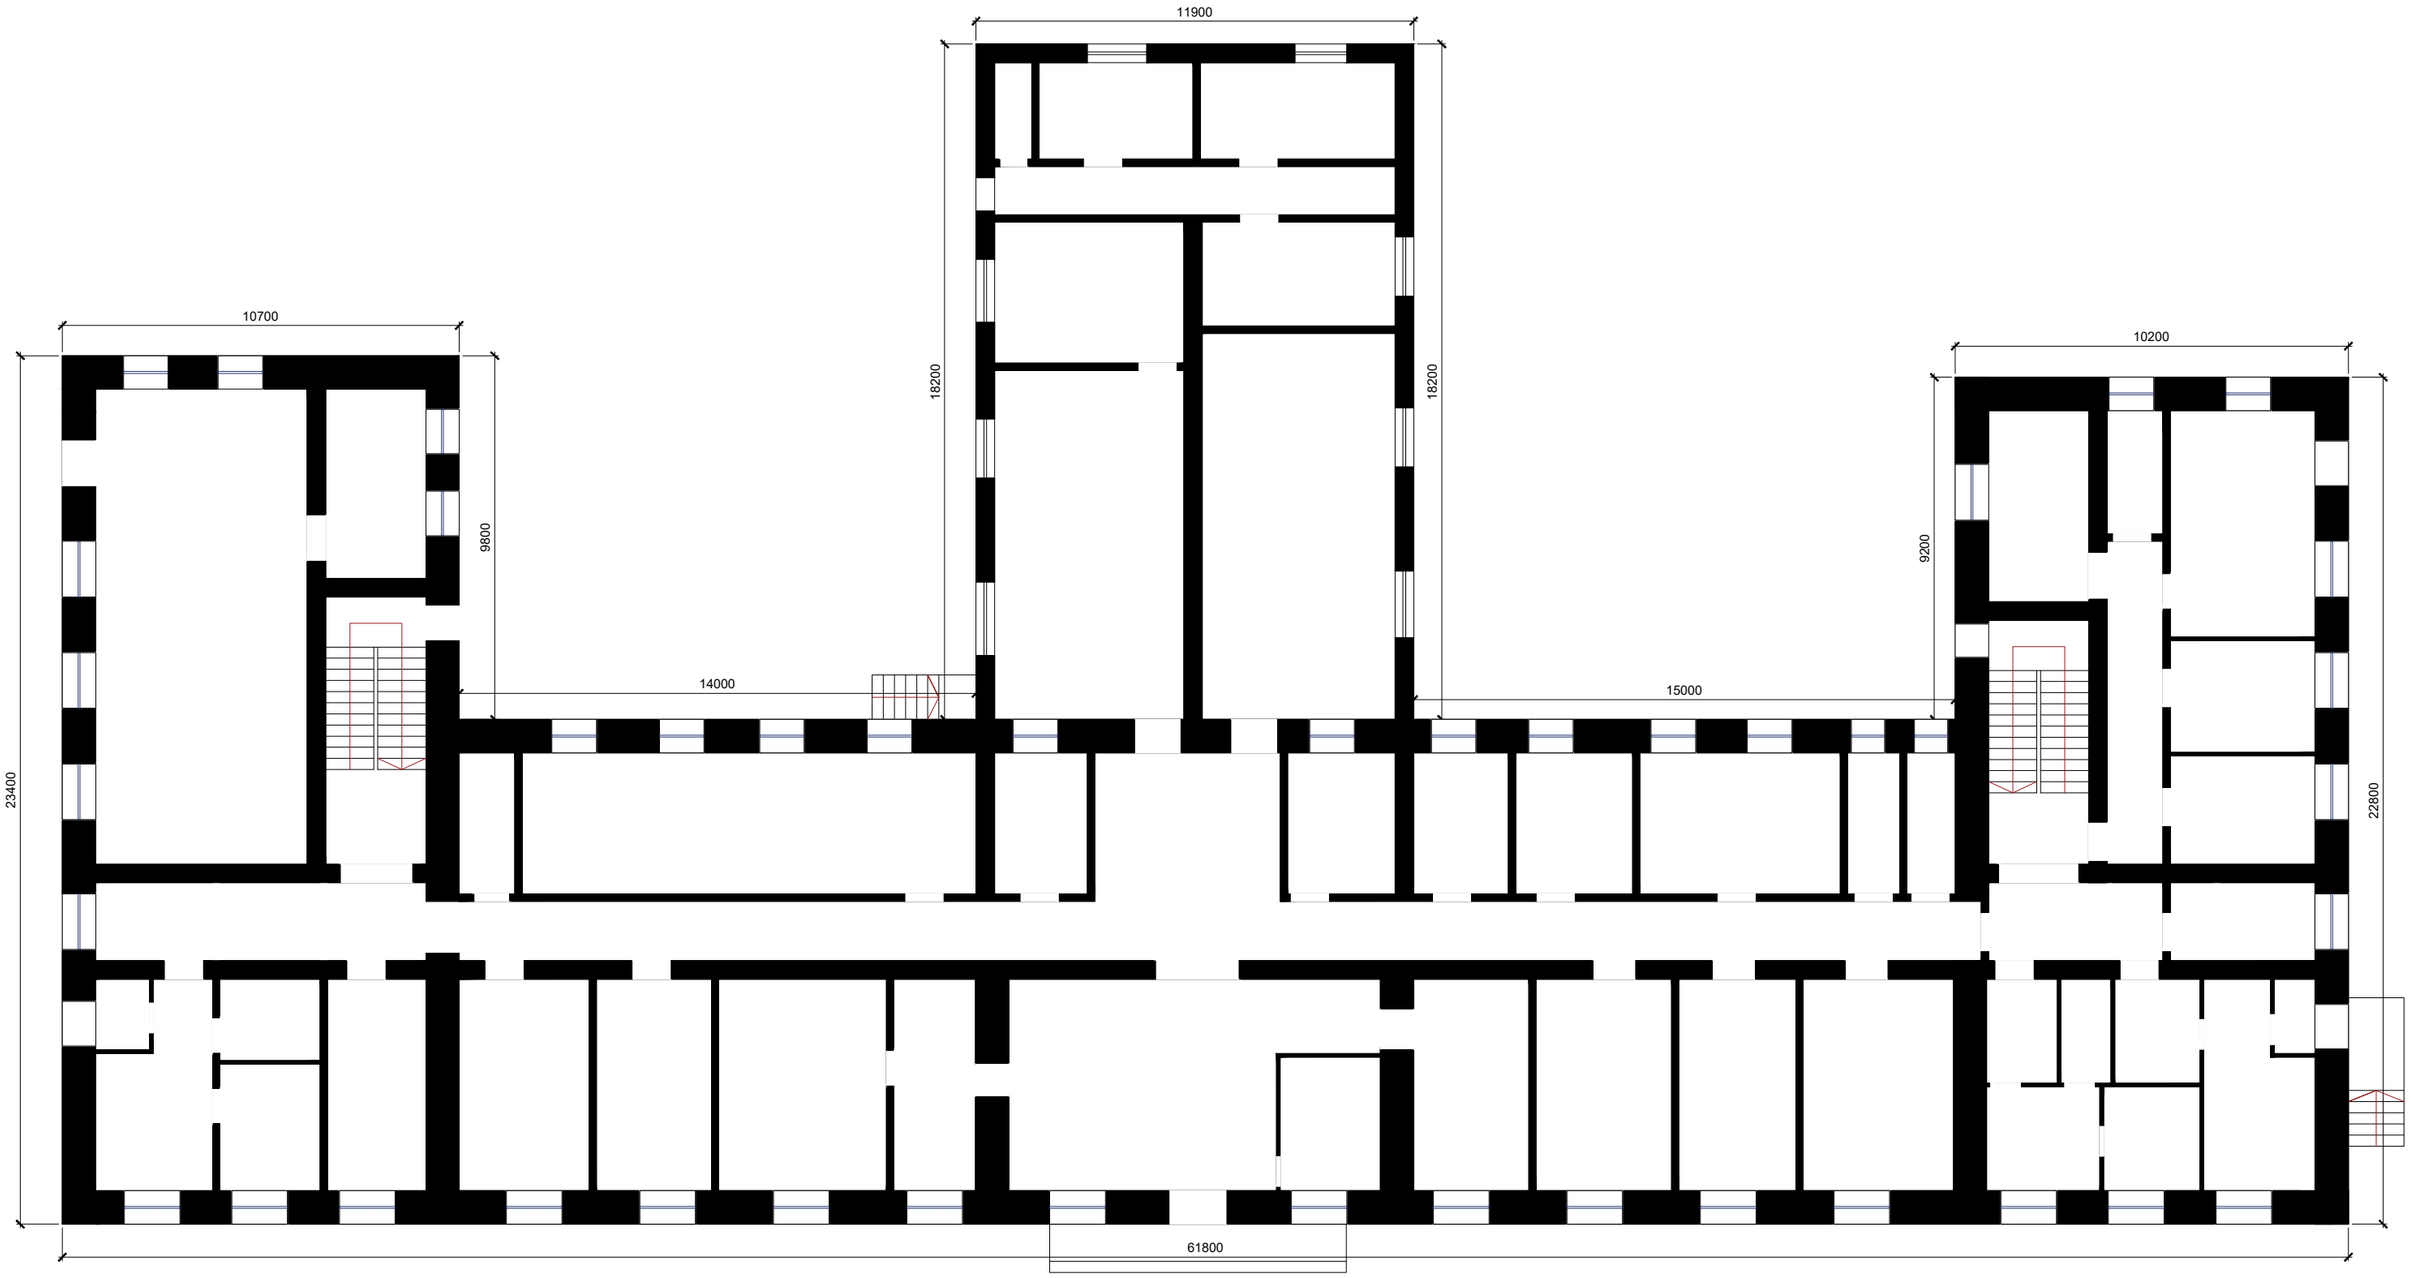

ԳՈՅՈՒԹՅՈՒՆ ՈՒՆԵՑՈՂ 1 ՀԱՐԿԻ ՀԱՏԱԿԱԳԻԾ

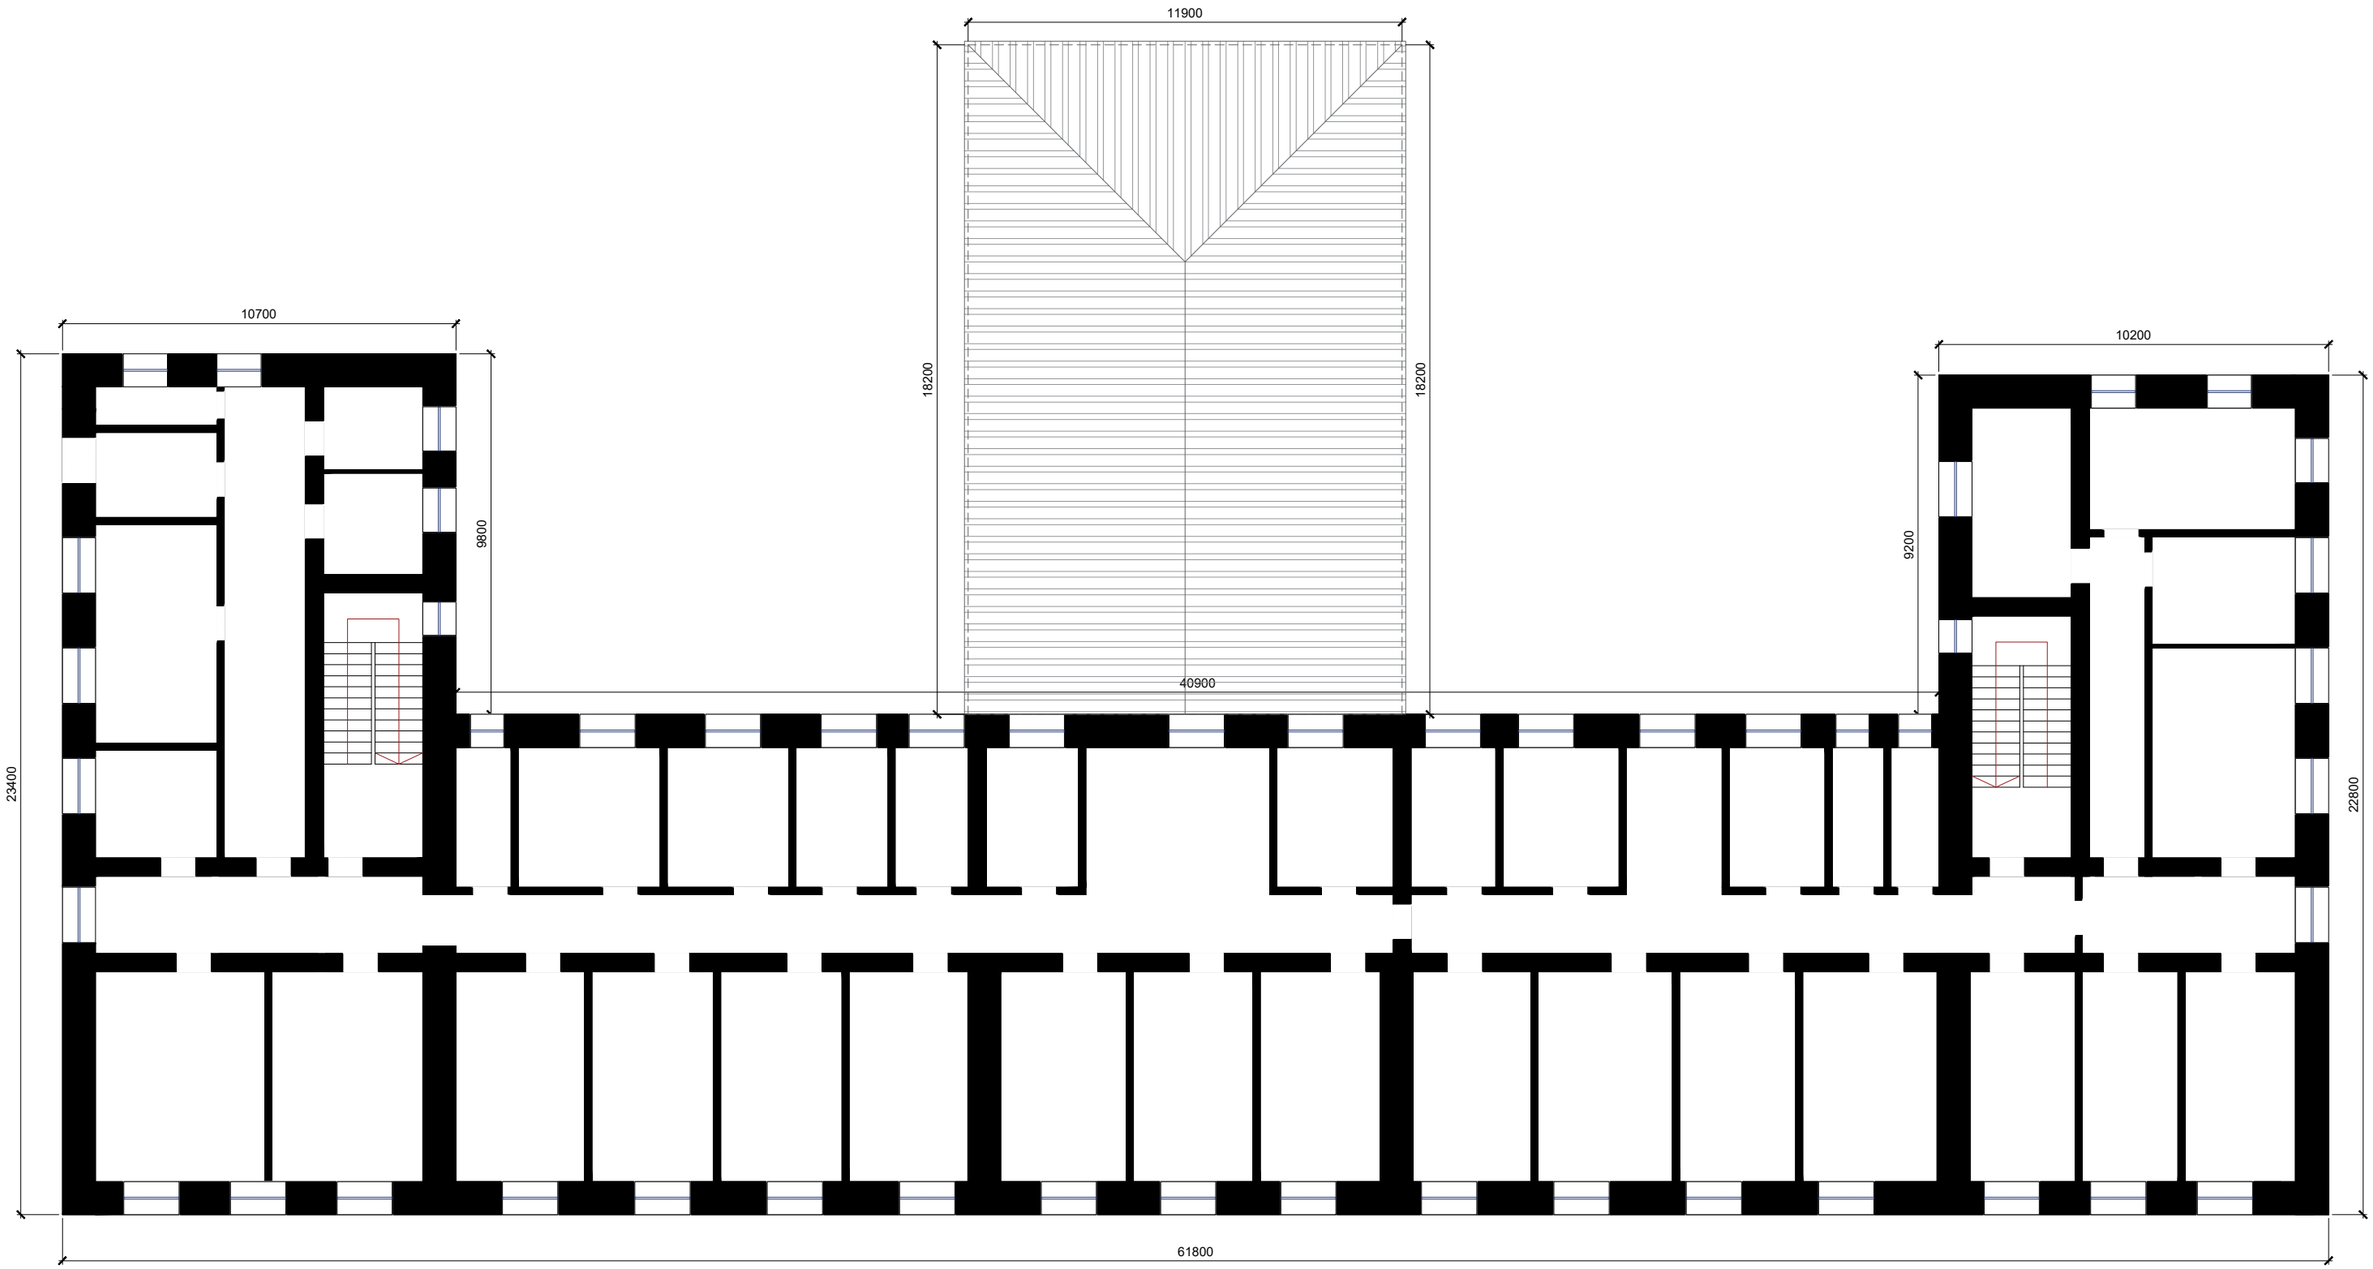

ԳՈՅՈՒԹՅՈՒՆ ՈՒՆԵՑՈՂ 2 ՀԱՐԿԻ ՀԱՏԱԿԱԳԻԾ

ԳԼԽԱՎՈՐ ՀԱՏԱԿԱԳԻԾ

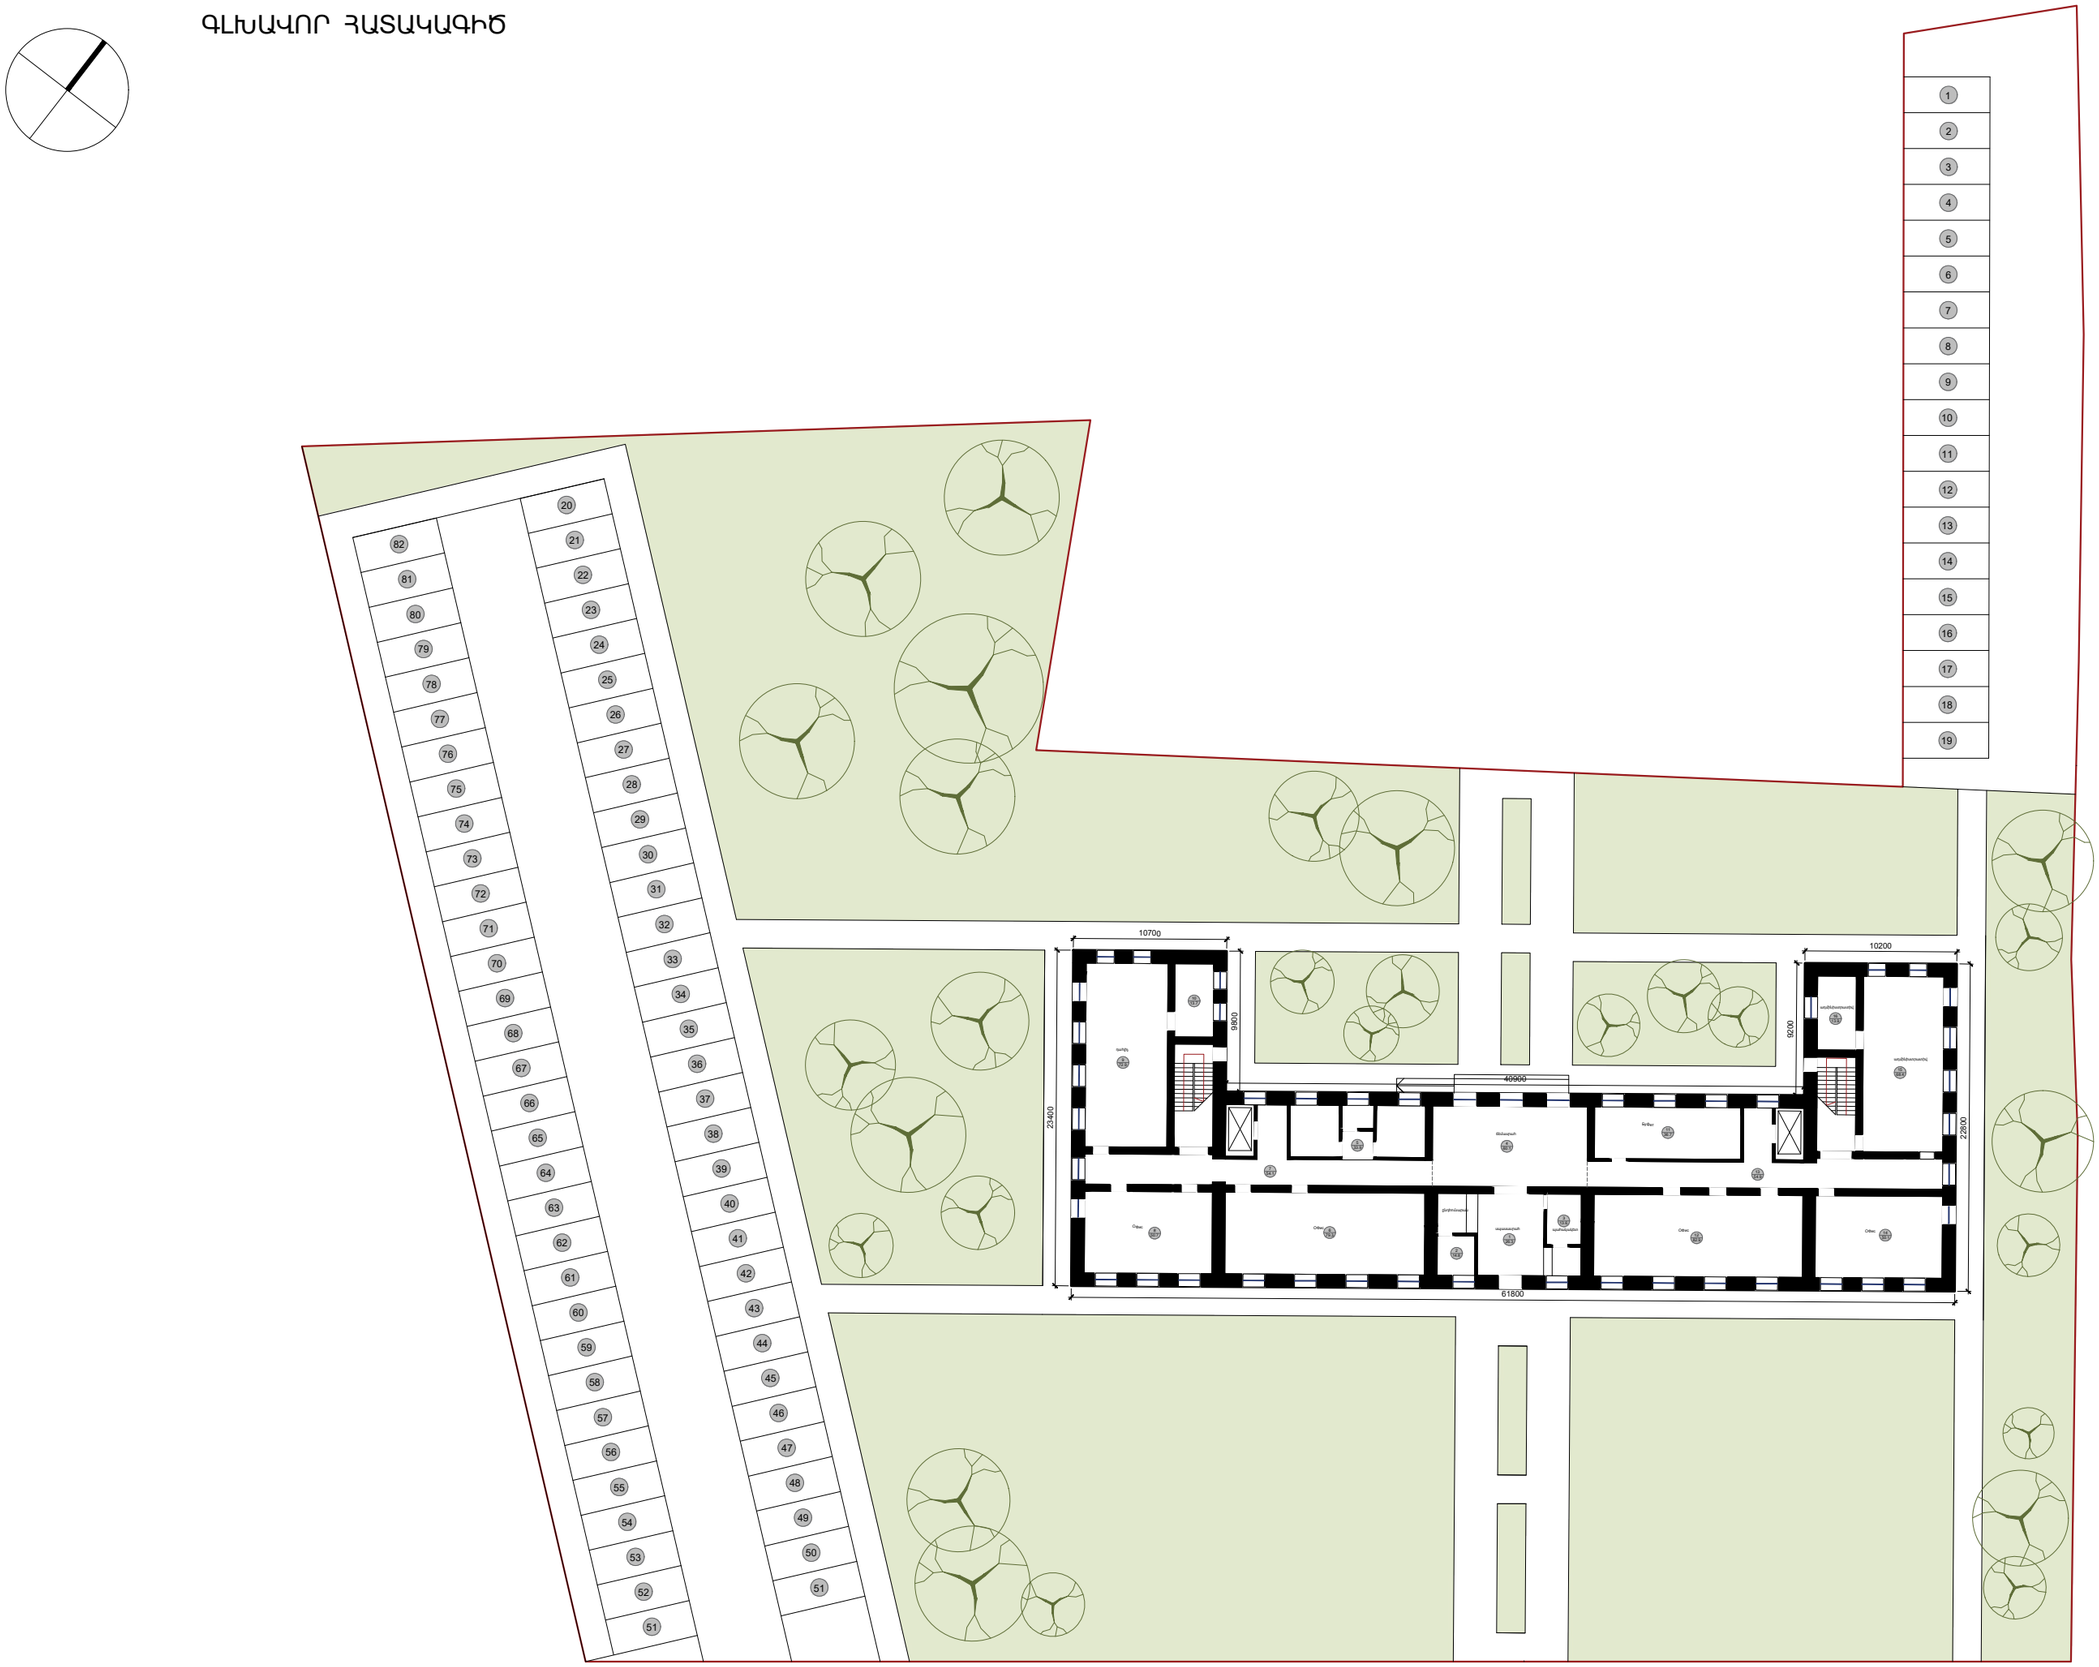

ԳԼԽԱՎՈՐ ՀԱՏԱԿԱԳԻԾ

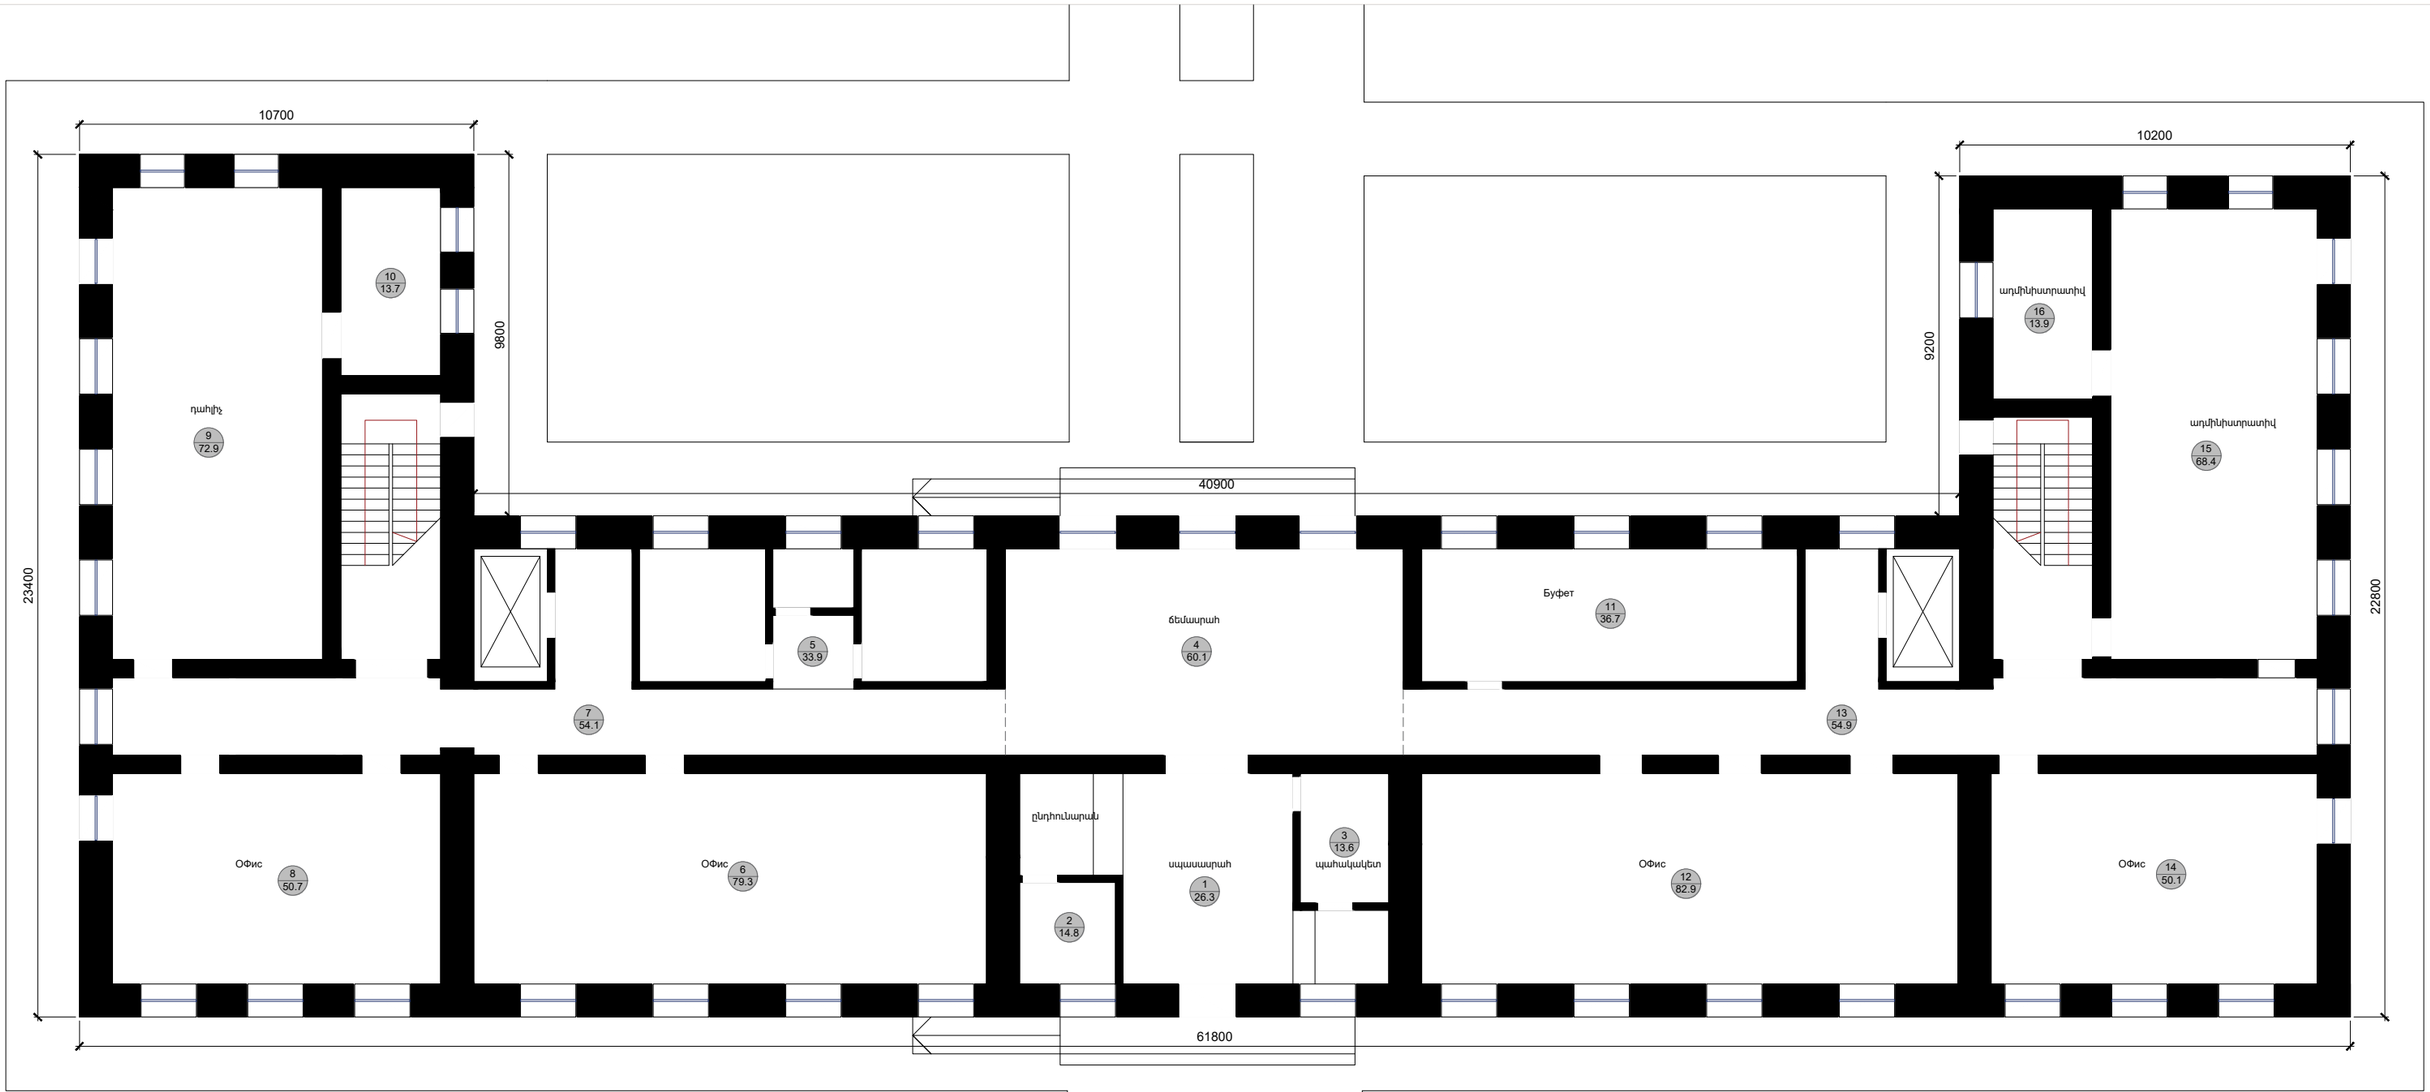

1	ՍՊԱՍԱՍՐԱՀ	26.3 $մ^2$
2	ԸՆԴՀՈՒՆԱՐԱՆ	14.8 $մ^2$
3	ՊԱՀԱԿԱԿԵՏ	13.6 $մ^2$
4	ՃԵՄԱՍՐԱՀ	60.1 $մ^2$
5	ՍԱՆՀԱՆԳՈՒՅՑՆԵՐ	33.9 $մ^2$
6	ՕԳԻՍԱՅԻՆ ՏԱՐԱԾՔ	79.3 $մ^2$
7	ՄԻՋԱՆՑՔ	54.1 $մ^2$
8	ՕԳԻՍԱՅԻՆ ՏԱՐԱԾՔ	50.7 $մ^2$
9	ԴԱՀՅԻՃ	72.9 $մ^2$
10	ՕԺԱՆԴԱԿ ՍԵՆՅԱԿ	13.7 $մ^2$
11	ԲՈՒՖԵՏ	36.7 $մ^2$
12	ՕԳԻՍԱՅԻՆ ՏԱՐԱԾՔ	82.9 $մ^2$
13	ՄԻՋԱՆՑՔ	54.9 $մ^2$
14	ՕԳԻՍԱՅԻՆ ՏԱՐԱԾՔ	50.1 $մ^2$
15	ԱԴՄԻՆԻՍՏՐԱՏԻՎ ՍԵՆՅԱԿ	68.4 $մ^2$
16	ԱԴՄԻՆԻՍՏՐԱՏԻՎ ՍԵՆՅԱԿ	13.9 $մ^2$
	ԱՍՏԻՃԱՆԱԿԱՆԴԱԿՆԵՐ	38.8 $մ^2$
	ԸՆԴՀԱՆՈՒՐ	**765.1 $մ^2$**

ԱՌԱՋԱՐԿՎՈՂ 1 ՀԱՐԿԻ ՀԱՏԱԿԱԳԻԾ

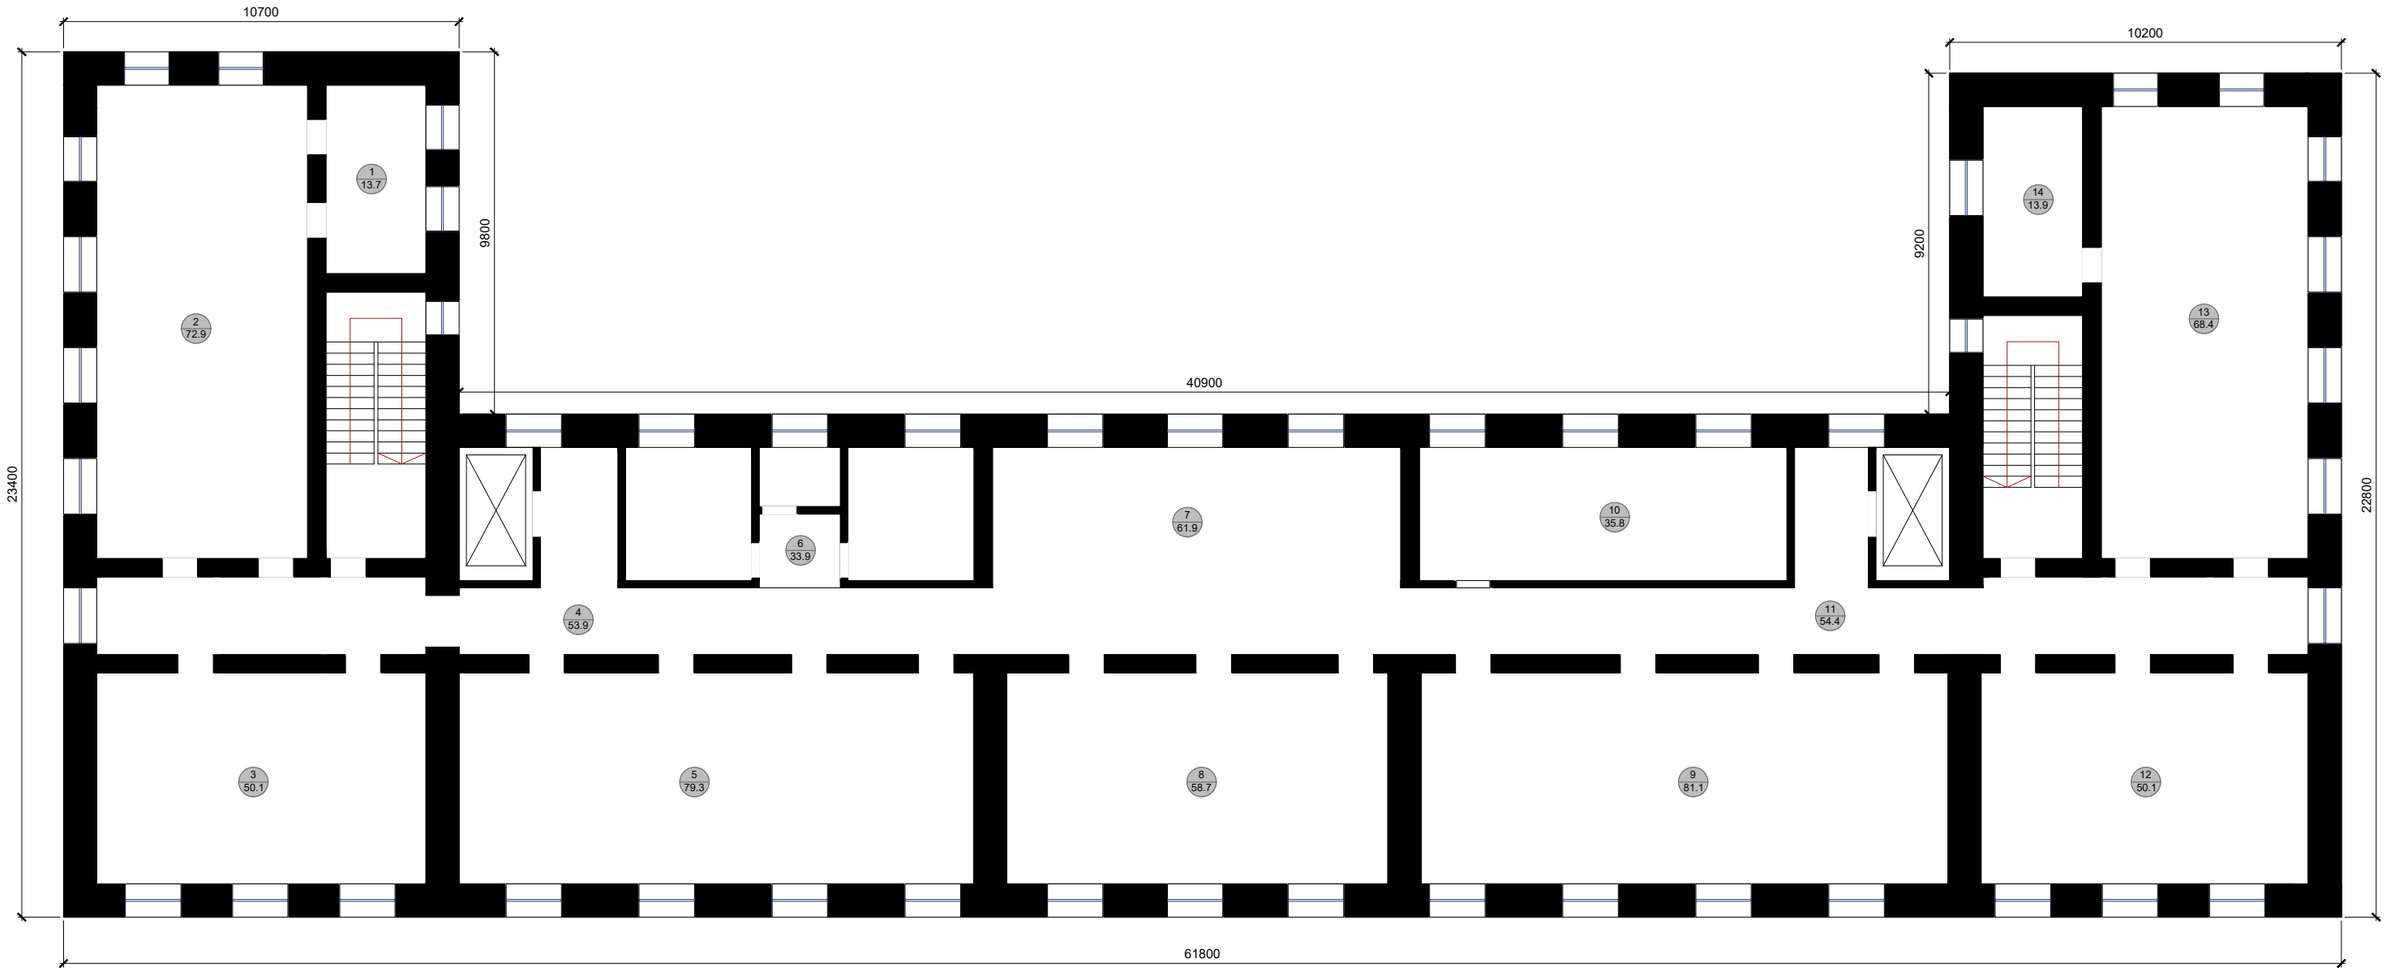

1	ՕԺԱՆԴԱԿ ՍԵՆՅԱԿ	13.7 $Մ^2$
2	ՕՖԻՍԱՅԻՆ ՏԱՐԱԾՔ	72.9 $Մ^2$
3	ՕՖԻՍԱՅԻՆ ՏԱՐԱԾՔ	50.1 $Մ^2$
4	ՄԻՋԱՆՑՔ	53.9 $Մ^2$
5	ՕՖԻՍԱՅԻՆ ՏԱՐԱԾՔ	79.3 $Մ^2$
6	ՍԱՆՀԱՆԳՈՒՅՑՆԵՐ	33.9 $Մ^2$
7	ՃԵՄԱՍՐԱՀ	61.9 $Մ^2$
8	ՕՖԻՍԱՅԻՆ ՏԱՐԱԾՔ	58.7 $Մ^2$
9	ՕՖԻՍԱՅԻՆ ՏԱՐԱԾՔ	81.1 $Մ^2$
10	ՕՖԻՍԱՅԻՆ ՏԱՐԱԾՔ	35.8 $Մ^2$
11	ՄԻՋԱՆՑՔ	54.4$Մ^2$
12	ՕՖԻՍԱՅԻՆ ՏԱՐԱԾՔ	50.1 $Մ^2$
13	ՕՖԻՍԱՅԻՆ ՏԱՐԱԾՔ	68.4 $Մ^2$
14	ՕԺԱՆԴԱԿ ՍԵՆՅԱԿ	13.9 $Մ^2$
	ԱՍՏԻՃԱՆԱՎԱՆԴԱԿՆԵՐ	38.8 $Մ^2$
	ԸՆԴՀԱՆՈՒՐ	**766.9 $Մ^2$**

ԱՌԱՋԱՐԿՎՈՂ 2 ՀԱՐԿԻ ՀԱՏԱԿԱԳԻԾ

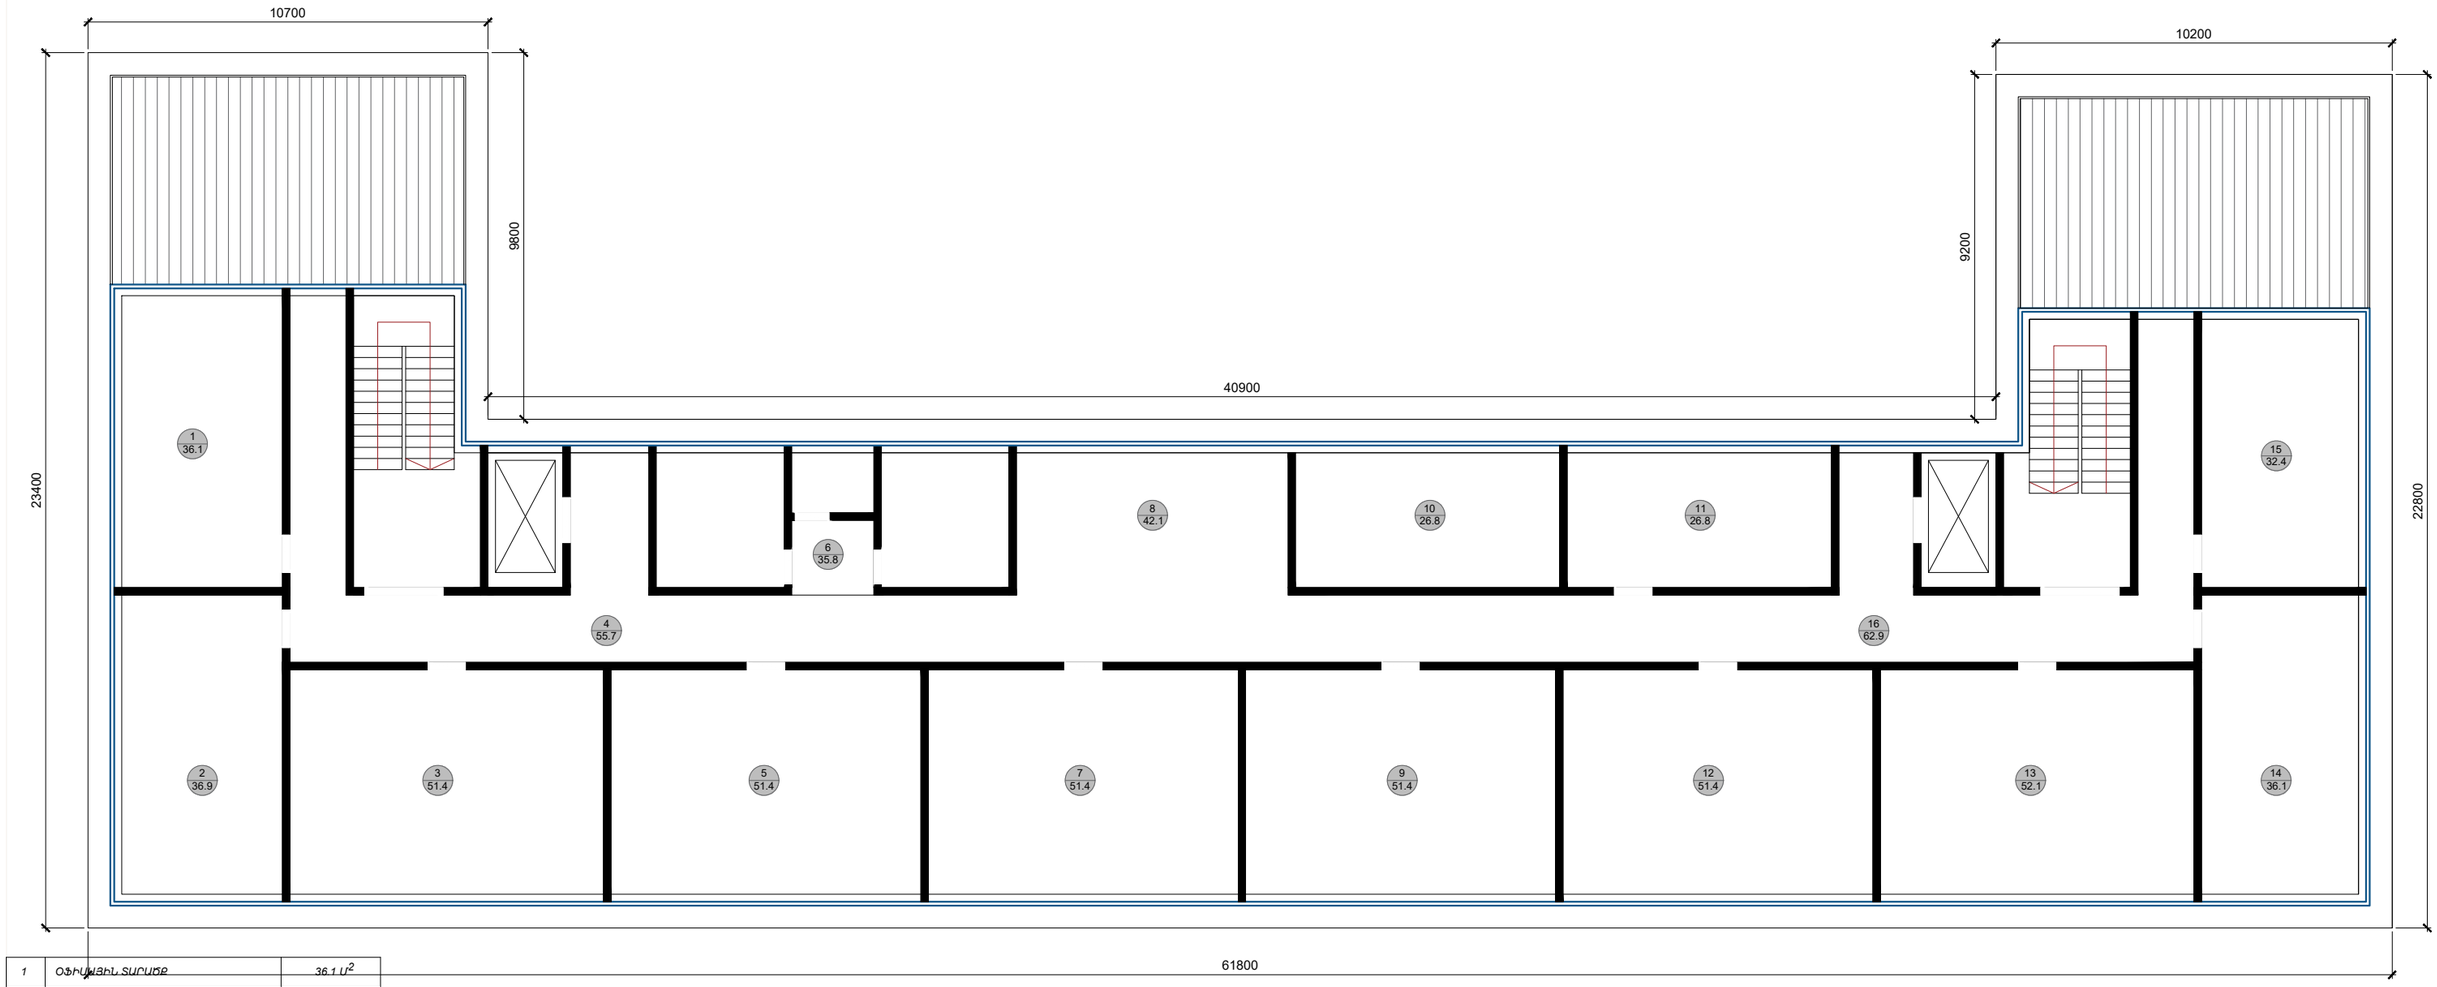

1	ՕԳԻՍԱՅԻՆ ՏԱՐԱԾՔ	36.1 $Մ^2$
2	ՕԳԻՍԱՅԻՆ ՏԱՐԱԾՔ	36.9 $Մ^2$
3	ՕԳԻՍԱՅԻՆ ՏԱՐԱԾՔ	51.4 $Մ^2$
4	ՄԻՋԱՆՑՔ	55.7 $Մ^2$
5	ՕԳԻՍԱՅԻՆ ՏԱՐԱԾՔ	51.4 $Մ^2$
6	ՍԱՆՀԱՆԳՈՒՅՑՆԵՐ	35.8 $Մ^2$
7	ՕԳԻՍԱՅԻՆ ՏԱՐԱԾՔ	54.1 $Մ^2$
8	ՃԵՄԱՍՐԱՀ	42.1 $Մ^2$
9	ՕԳԻՍԱՅԻՆ ՏԱՐԱԾՔ	51.4 $Մ^2$
10	ՕԳԻՍԱՅԻՆ ՏԱՐԱԾՔ	26.8 $Մ^2$
11	ՕԳԻՍԱՅԻՆ ՏԱՐԱԾՔ	26.8 $Մ^2$
12	ՕԳԻՍԱՅԻՆ ՏԱՐԱԾՔ	51.4 $Մ^2$
13	ՕԳԻՍԱՅԻՆ ՏԱՐԱԾՔ	52.1 $Մ^2$
14	ՕԳԻՍԱՅԻՆ ՏԱՐԱԾՔ	36.1 $Մ^2$
15	ՕԳԻՍԱՅԻՆ ՏԱՐԱԾՔ	32.4 $Մ^2$
16	ՄԻՋԱՆՑՔ	62.9 $Մ^2$
	ԱՍՏԻՃԱՆԱՎԱՆԴԱԿՆԵՐ	38.8 $Մ^2$
	ՏԵՐԱՍՍԱՆԵՐ	106.4 $Մ^2$
	ԸՆԴՀԱՆՈՒՐ	**848.6 $Մ^2$**

ԱՌԱՋԱՐԿՎՈՂ 3 ՀԱՐԿԻ ՀԱՏԱԿԱԳԻԾ

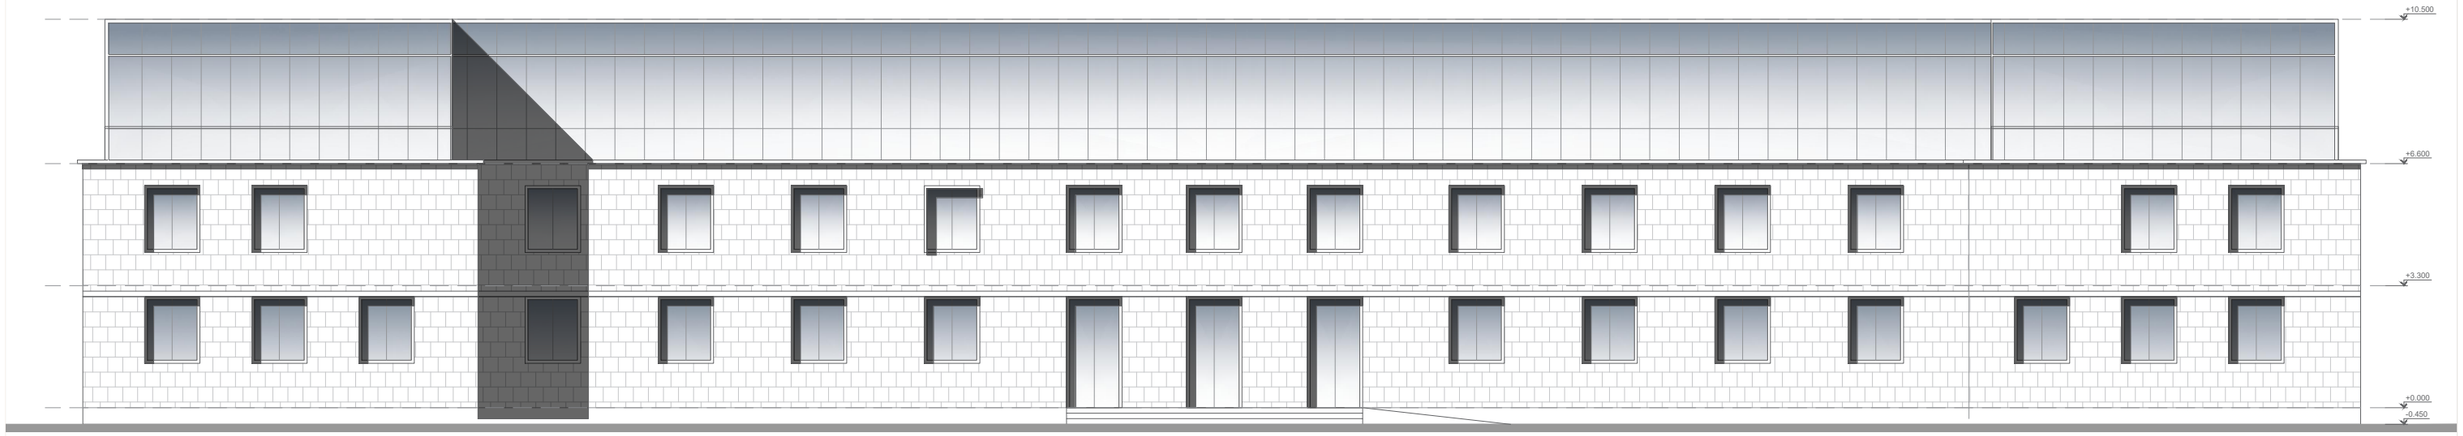

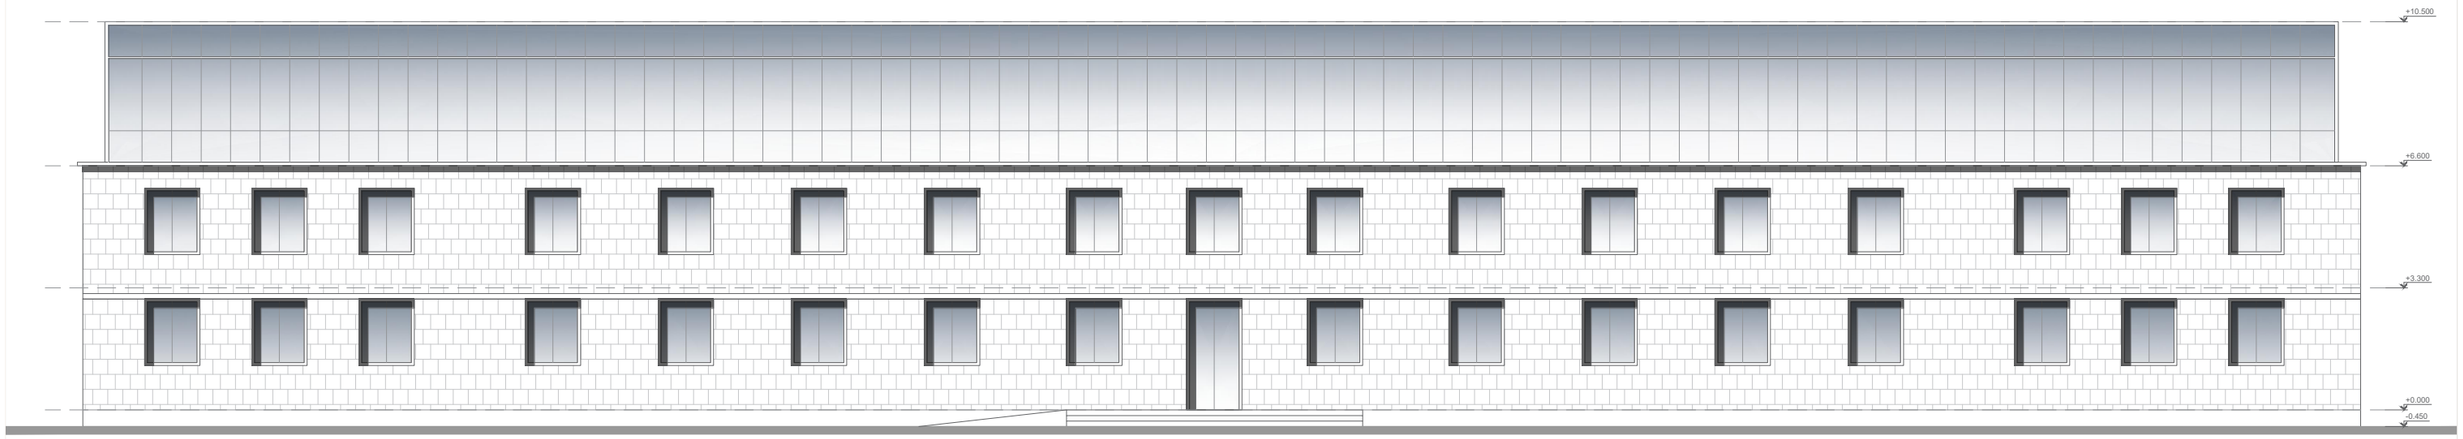

ԳԼՂԱՎՈՐ ԵՎ ԲԱԿԱՅԻՆ ՃԱԿԱՏՆԵՐ

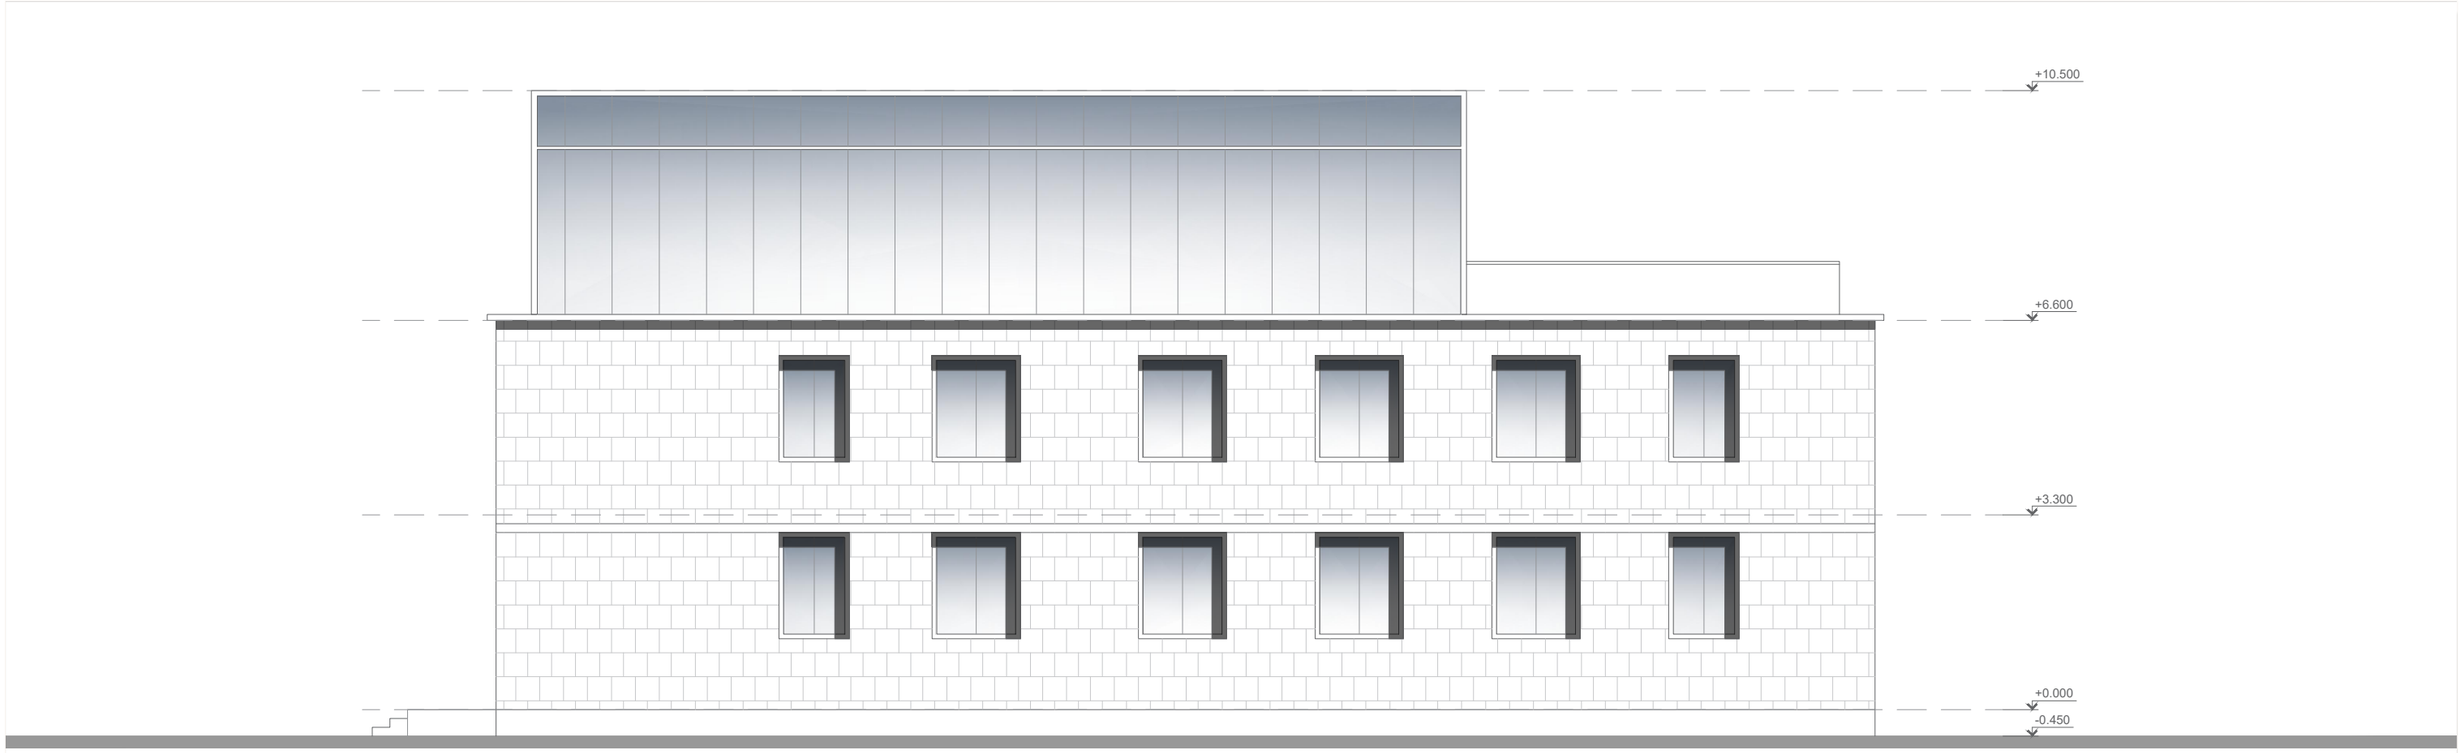

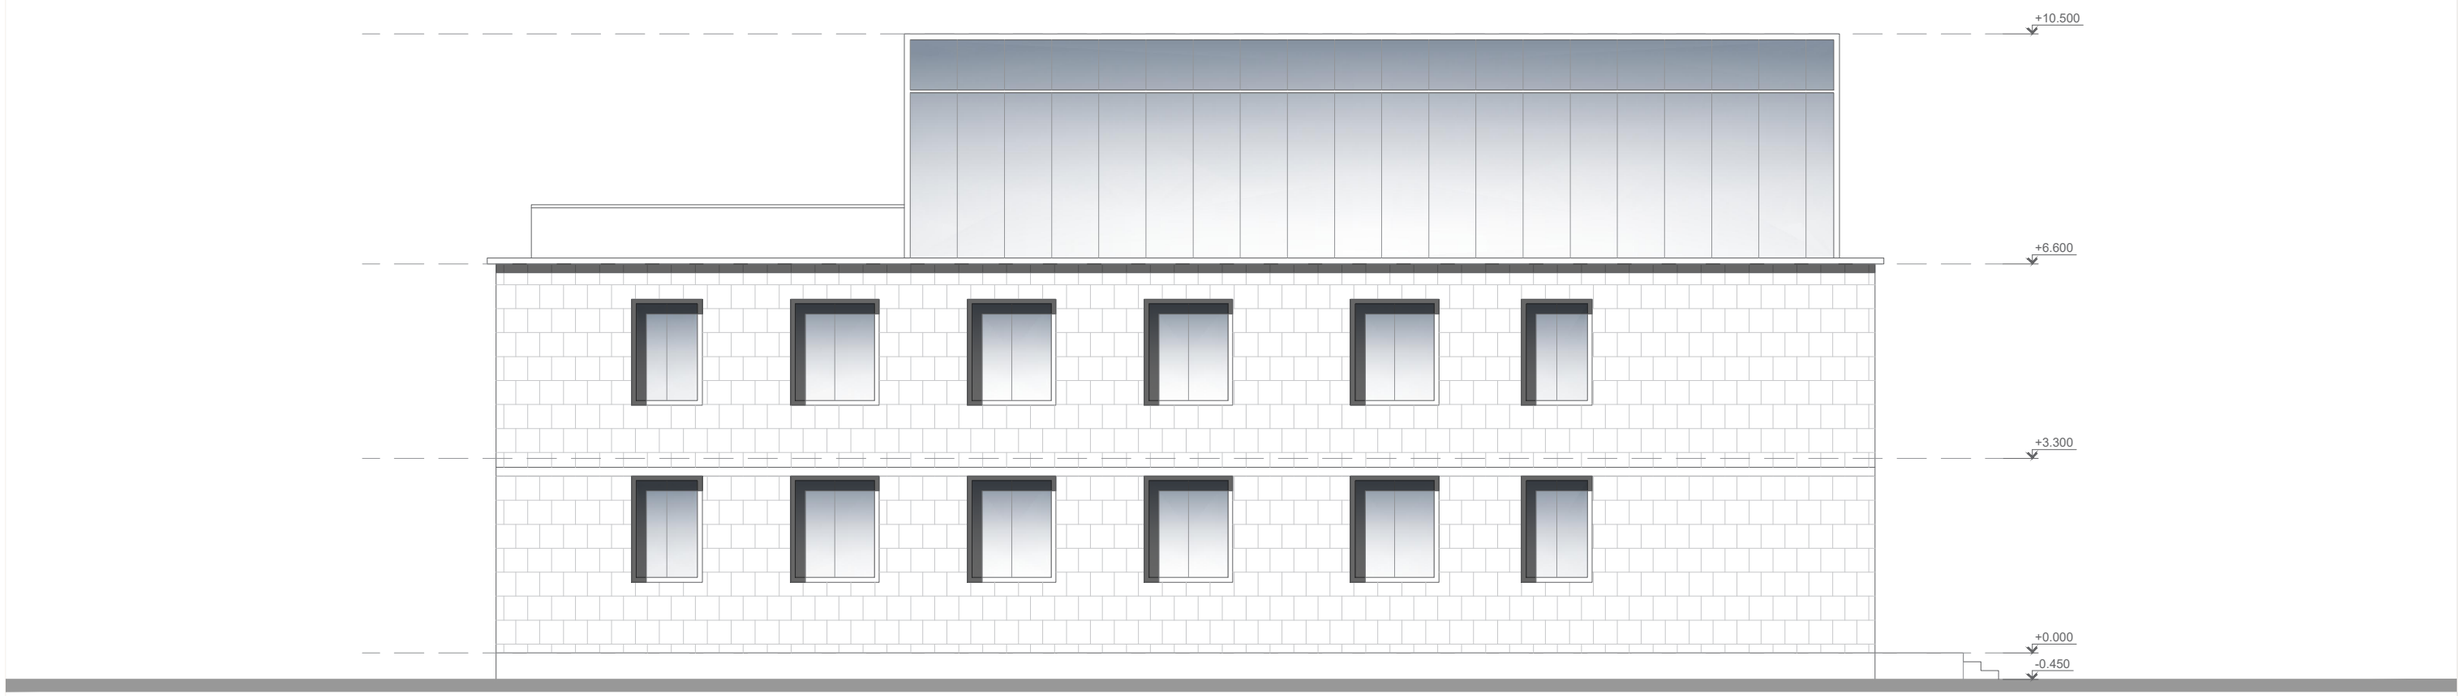

ԿՈՂԱՅԻՆ ՃԱԿԱՏՆԵՐ

	ՀՈՂԱՄԱՍԻ ՀԱՏԱԿԱԳԻԾ		Ձև 1
Սեփականատեր	Կոտայքի մարզ, Նաիրի համայնք, գյուղ Քասախ,	Հաստատում եմ « »	2025 թ.
Հայաստանի Հանրապետություն	Վ. Սարգսյան 8/4	Համայնքի ղեկավար	Կ. Տ.
		Նորայր Սարգսյան	

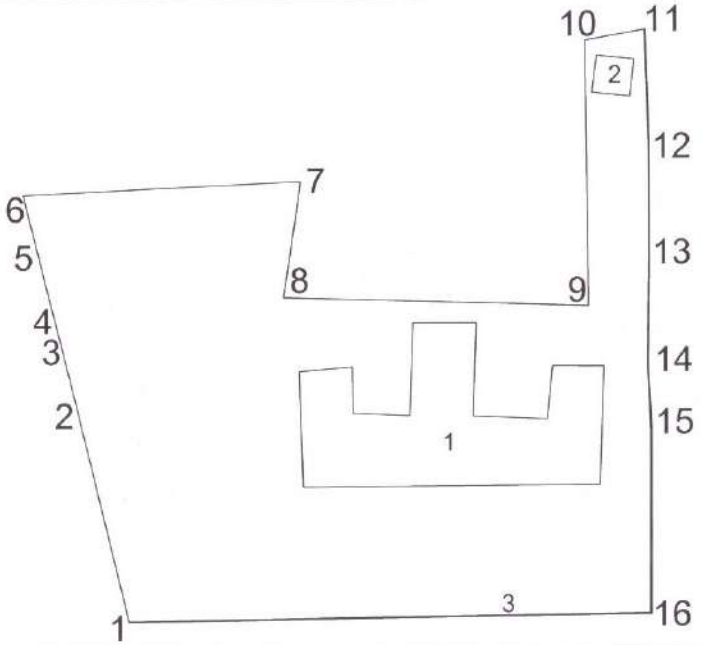

Մակերես (հա)	0.874	Հողամասի				Մասշտաբ 1:1000			
Ծածկագիր	07-065-0036-0001	Շրջա-դարձման (շեղման) կետեր	Կոորդինատներ		Գծային չափեր (մ)	Որակավորում ունեցող անձ		Գևորգ Խուդավերդյան	
Նպատակային նշանակություն	Բնակավայրերի					Որակավորման վկայականի համարը		0194	
			X	Y		Ստորագրություն			
Գործառնական նշանակություն	Հասարակական կառուցապատման	1	4455928.80	8453466.17	43.73	Իրավաբանական անձի անվանումը		«Տավուշ հոլդինգ» ՍՊԸ	
		2	4455956.44	8453432.28	12.47	ՀՎՀՀ		07405006	
		3	4455964.32	8453422.62	5.28	Ստորագրություն			
		4	4455967.66	8453418.52	15.14	ամիս համաթիվ	չափագրության	03.04.2025թ.	Կ. Տ.
		5	4455977.23	8453408.79	10.37		հատակագծի կազմման	03.04.2025թ.	
		1	4455983.78	8453398.75	55.03				